
SBS GRANULE-SURFACED ROOFING MEMBRANE OR PVC, 20-YR.
CLASS "A" FIRE-RATED
TWO-PLY SYSTEM CONSISTING OF LIBERTY™ SBS SELF-ADHERING BASE/PLY SHEET ADHERED TO A PRIMED PLYWOOD DECK AND LIBERTY™ SBS SELF-ADHERING CAP SHEET. USING BOTH LIBERTY™ ASPHALT PRIMER AND LIBERTY™ PREMIUM SBS FLASHING CEMENT ACCESSORIES; OR SIMILAR.


GENERAL CONTRACTOR SHALL VERIFY IF A LAYER OF #30 NON-PERFORATED ROOFING FELT, ALL SHEET METAL WITH ROOF JACKS, CRICKETS, SADDLES, AND/OR FLASHING/EDGE STRIPS.

FASTENERS FOR THE ROOFING SHALL BE CORROSION RESISTANT PER CRC R905.2.5.

OPERABLE SKYLIGHTS SHALL BE PROTECTED BY A NONCOMBUSTIBLE MESH SCREEN WITH OPENINGS NO LARGER THAN 1/8 INCH. [R337.8.2.2]

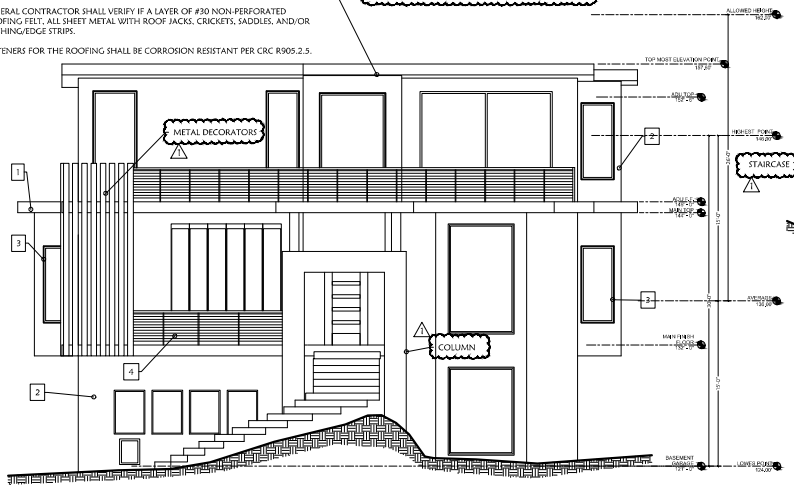

PROPOSED FRONT ELEVATION
03 SCALE 1 : 3/16"

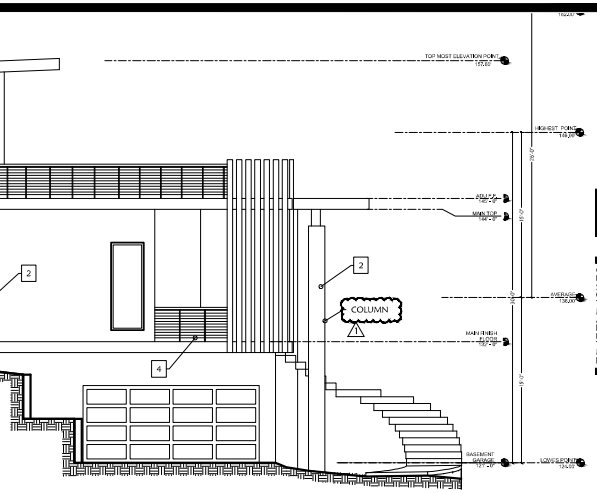

PROPOSED LEFT ELEVATION
02 SCALE 1 : 3/16"

ENERGY INSULATION:

1. INSTALL INSULATION IN WALLS BETWEEN CONDITIONED AND UNCONDITIONED SPACE PER TITLE 24 OR PER CF-1R PERFORMANCE].
2. INSTALL INSULATION AT CEILINGS EXPOSED TO UNCONDITIONED SPACE WITH MINIMUM 1" AIR SPACE BETWEEN INSULATION AND UNDERSIDE OF ROOF SHEATHING FOR VENTILATION.
3. INSULATION SHALL BE INSTALLED CORRECTLY WITH NO GAPS GREATER THAN 1/8" [USE FOAM]; NO VOIDS; NO COMPRESSIONS DEEPER THAN ¼" [LESS THAN 10% OF CAVITY AREA], WITH INSULATION COMPLETELY FILLING THE CAVITY AND MINIMUM 90 % IN CONTACT WITH ALL 6 CAVITY SURFACES (FLUSH WITH THE FACE OF FRAMING MEMBERS). INSULATION SHALL BE CUT TO FIT AROUND WIRING OR PLUMBING, OR SPLIT TO ENCAPSULATE WIRING OR PLUMBING. RECOMMEND USING UNFACED BATTS, BUT IF FACED, THE VAPOR RETARDER SHALL FACE INTO THE CONDITIONED SPACE.

PROTECT THE UNDERFLOOR AREA OF ELEVATED OR OVERHANGING BUILDINGS, EXPOSED UNDERSIDE OF EXTERIOR PORCH CEILINGS, THE EXPOSED UNDERSIDE OF CANTILEVERED FLOOR PROJECTIONS, AND THE UNDERSIDE OF OVERHANGING APPENDAGES WITH NONCOMBUSTIBLE MATERIAL, FIRE RETARDANT TREATED WOOD, IGNITION RESISTANT MATERIAL, OR ADD A 5/8" LAYER OF TYPE X GYPSUM BEHIND THE EXTERIOR COVERING ON THE UNDERSIDE OF THE DECK, OR AS PART OF A 1-HOUR ASSEMBLY. [R337.7.7, 8, 9 & 10]


ALL EXTERIOR WINDOWS MUST HAVE THE EXTERIOR PANE TEMPERED. HAVE NOT LESS THAN A 20-MINUTE FIRE-RESISTANCE RATING, OR BE TESTED TO SFM STANDARD 12-7A-2. [R337.8.2.1]

EXTERIOR FINISHES:


1. SBS GRANULE-SURFACED ROOFING MEMBRANE OR PVC, 20-YR. CLASS "A" FIRE-RATED TWO-PLY SYSTEM CONSISTING OF LIBERTY™ SBS SELF-ADHERING BASE/PLY SHEET ADHERED TO A PRIMED PLYWOOD DECK AND LIBERTY™ SBS SELF-ADHERING CAP SHEET. USING BOTH LIBERTY™ ASPHALT PRIMER AND LIBERTY™ PREMIUM SBS FLASHING CEMENT ACCESSORIES; OR SIMILAR.

 GENERAL CONTRACTOR SHALL VERIFY IF A LAYER OF #30 NON-PERFORATED ROOFING FELT, ALL SHEET METAL WITH ROOF JACKS, CRICKETS, SADDLES, AND/OR FLASHING/EDGE STRIPS.

 FASTENERS FOR THE ROOFING SHALL BE CORROSION RESISTANT PER CRC R905.2.5.
 COOL ROOF, PROVIDE ROOF SHEATHING WITH RADIANT BARRIER, CHARCOAL LAMINATED ARCHITECTURAL ROOF SHINGLES
2. 7/8" MIN. 3-COAT STUCCO OVER 2 WIRE LATH O/2 LAYERS OF GRADE "D" BLDG PAPER SMOOTH TEXTURE. SWISS COFFEE COLOR TYP.
3. BLACK VINYL / WINDOWS AND DOORS TYP.
4. 42" CABLE RAILING RAILING TYP.

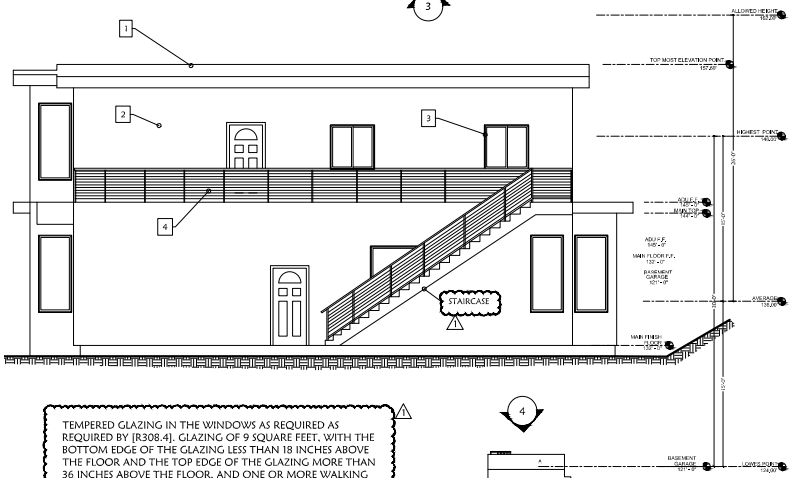

TEMPERED GLAZING IN THE WINDOWS AS REQUIRED AS REQUIRED BY [R308.4]. GLAZING OF 9 SQUARE FEET, WITH THE BOTTOM EDGE OF THE GLAZING LESS THAN 18 INCHES ABOVE THE FLOOR AND THE TOP EDGE OF THE GLAZING MORE THAN 36 INCHES ABOVE THE FLOOR, AND ONE OR MORE WALKING SURFACES ARE WITHIN 36 INCHES, MEASURED HORIZONTALLY AND IN A STRAIGHT LINE OF THE GLAZING, MUST BE PROTECTED WITH SAFETY GLASS. [R308.4.3]

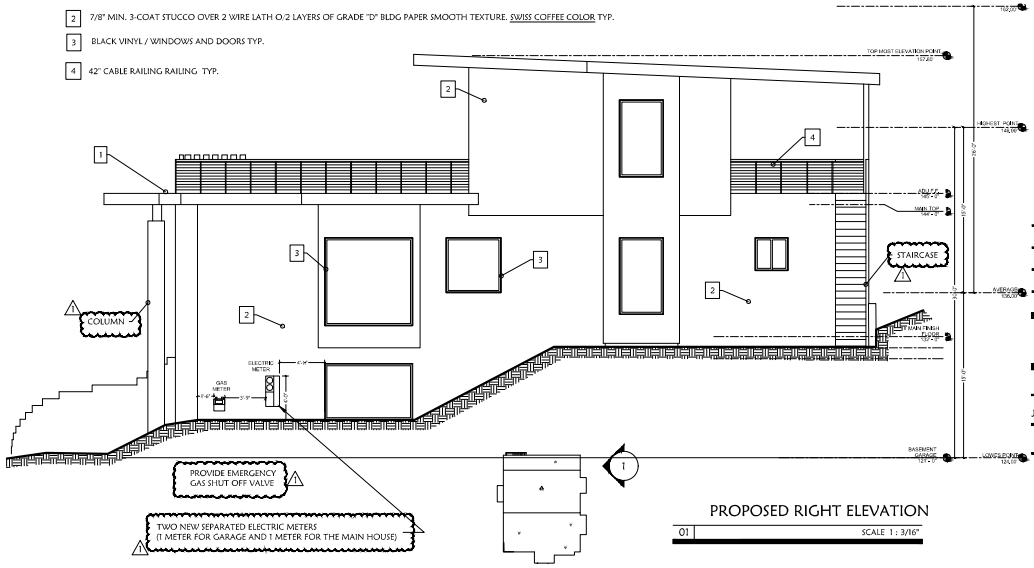

PROPOSED RIGHT ELEVATION
01 SCALE 1 : 3/16"

HzR HOME DESIGNERS INC.
541 W CAPITOL EXPWY. SUITE 10 PMB 256, SAN JOSE, CA 95136
hzr.designers@gmail.com 408.613.6201

COPYRIGHT: THESE PLANS SPECIFICATIONS, DETAILS, ANY DRAWING AND DESIGNS ARE THE SOLE PROPERTY OF HzR HOME DESIGNERS. CONSTRUCTION IS LIMITED TO ONE TIME USE FOR THE PROPERTY NAMED HERE IN. THESE PAGES MAY NOT BE DISPLAYED, COPIED, OR USED IN ANY WAY WITHOUT THE EXPRESS WRITTEN PERMISSION OF HZR HOME DESIGNERS. THESE PLANS HAVE BEEN DRAWN TO COMPLY WITH THE CLIENTS SPECIFICATIONS AND ANY CHANGES MADE TO THEM AFTER PRINTS ARE MADE SHALL BE DONE AT THE CLIENTS EXPENSE.

PROPOSED NEW RESIDENCE FOR:
"THE PRAIKA LLC RESIDENCE"
15261 NORTON RD SARATOGA CA 950700
APN: 517-14-0081

Authorization Sign
Silverio H. Madera / Designer
hzr.designers@gmail.com
408.613.6201

Nº	Revision	Date
1	Building comms.	6.30.25
2		
3		

SHEET NAME:
PROPOSED ELEVATIONS

Project No. H-2404
Sheet No. A5.0
Date July 03, 2025
Scale AS SHOWN
CITY STAMP:

C:\Users\ve\My Drive\Hzr Home Designers\4 Projects 2024\2404- 15261 Norton Rd Saratoga CA 95070\2025\2404- CAD\2404- A1.1 PROPOSED FLOOR PLAN 5 - resp to comme